
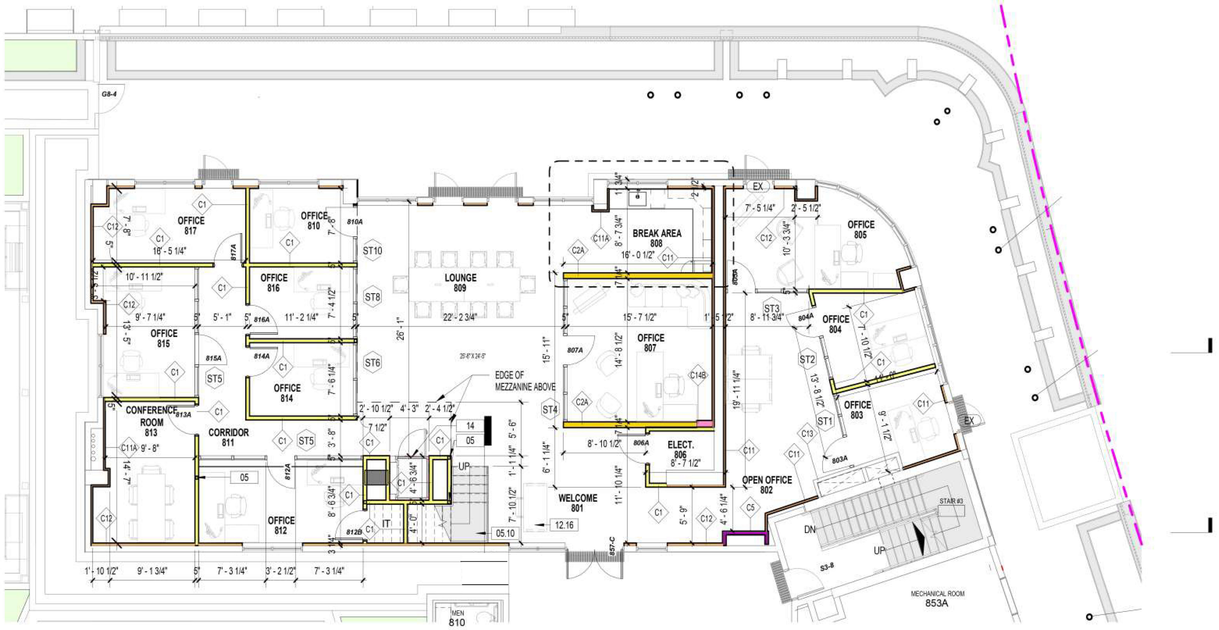


8TH FLOOR PLAN

SCALE: 1/8" = 1'-0"

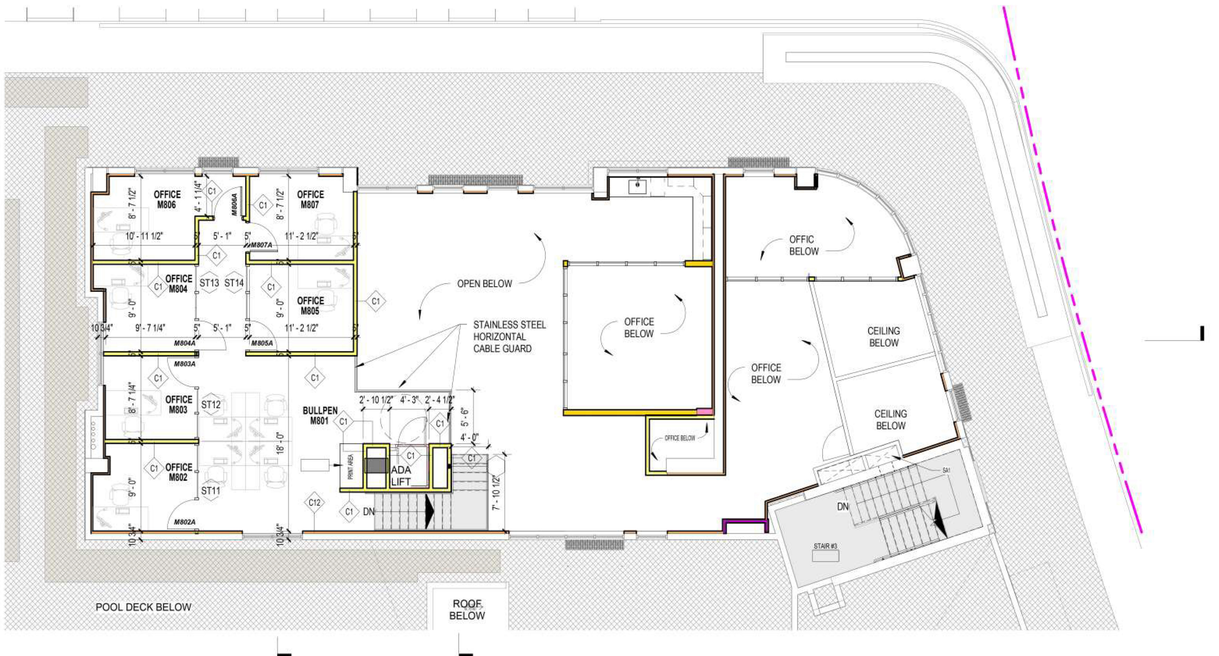

8TH FLOOR MEZZANINE PLAN

SCALE: 1/8" = 1'-0"

REVISIONS	BY

National Glass & Construction
7781 NW 54th Street Doral FL 33166
Ph. (305) 599 09 09 - Fax. (305) 591 81 88
www.ngtglass.net

AM American Consulting, Inc.
10300 SW 72nd Street, Suite 455,
Miami, FL 33184 / Ph (786) 219 9490
Email: contact@amamericanconsulting.com
www.amamericanconsulting.com

PROJECT: JBL Asset Management TI

1818 PARK HOLLYWOOD FLORIDA 33020

INTERIOR GLAZING PARTITIONS

Date: 9/8/2024

Scale: AS SHOWN

Drawn: Y. FEITO

Job:

Sheet: SD 2

Of ____ Sheets