
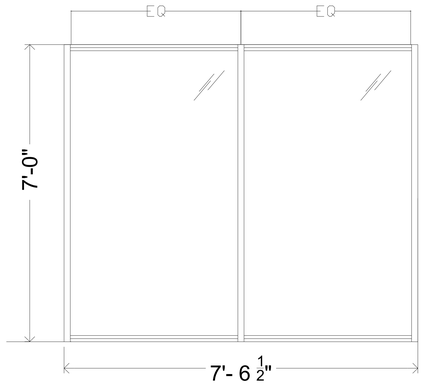



5 **ST6**

SCALE: 1/4" = 1'-0"

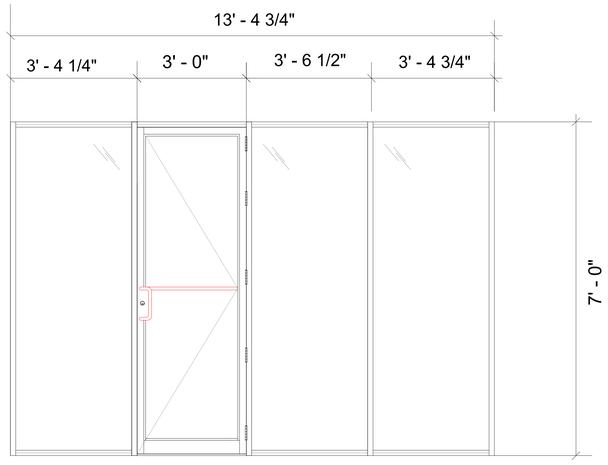


6 **ST7**

SCALE: 1/4" = 1'-0"

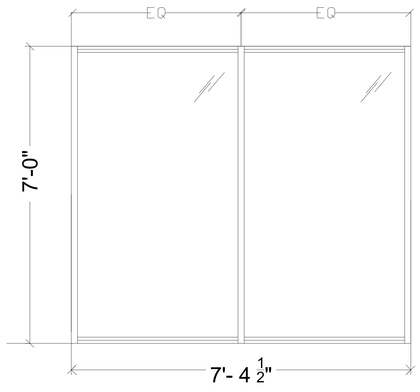

7 **ST8**

SCALE: 1/4" = 1'-0"

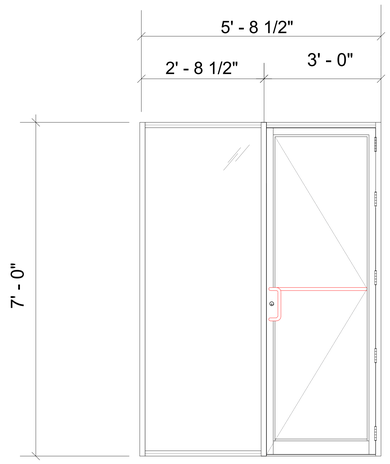

8 **ST9**

SCALE: 1/4" = 1'-0"

REVISIONS	BY

National Glass & Construction
7781 NW 56th Street - Doral Fl. 33166
Ph. (305) 599 09 09 - Fax. (305) 591 81 88
www.nationalglass.net

AM American Consulting, Inc.
10300 SW 72nd Street, Suite 455
Miami, FL 33184 / Ph (786) 219 9490
Email: contact@amamericanconsulting.com
www.amamericanconsulting.com

PROJECT: JBL ASSET MANAGEMENT TI
1818 PARK HOLLYWOOD, FLORIDA, 33020
INTERIOR GLAZING PARTITIONS

Date: 9/8/2024
Scale: AS SHOWN
Drawn: Y. FEITO
Job:
Sheet: SD – 4
Of ____ Sheets