
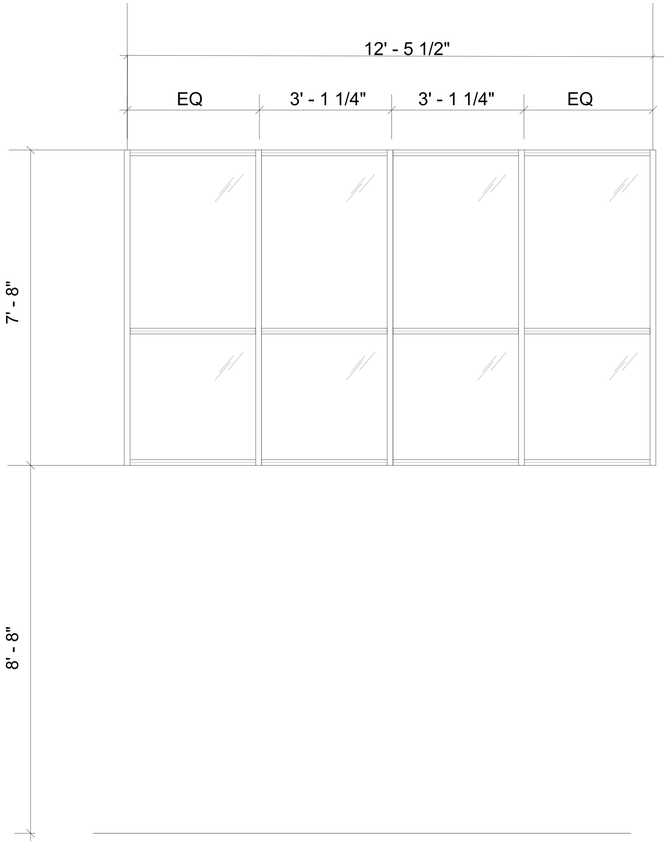


13 **ST4B**


SCALE: 1/4" = 1'-0"

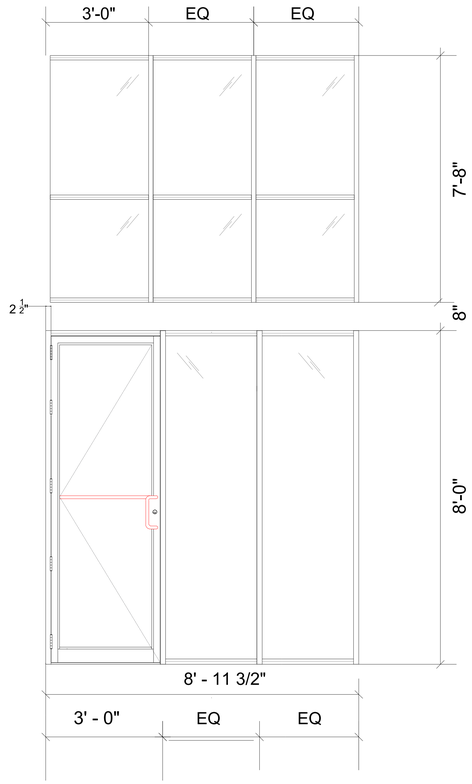

14 **ST3 & ST3A**

SCALE: 1/4" = 1'-0"

17
A-5.1.05

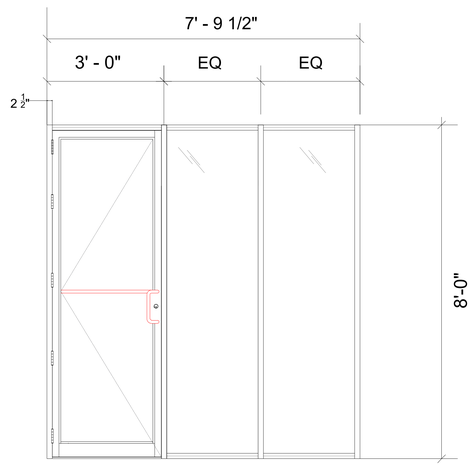

15 **ST2**

SCALE: 1/4" = 1'-0"

REVISIONS | BY

National Glass & Construction
7781 NW 56th Street - Doral Fl. 33166
Ph. (305) 599 09 09 - Fax. (305) 591 81 88
www.natlglass.net

AM American Consulting, Inc.
10300 SW 72nd Street, Suite 455,
Miami, FL 33184 / Ph (786) 219 9490
Email: contact@amamericanconsulting.com
www.amamericanconsulting.com

PROJECT: JBL ASSET MANAGEMENT TI
1818 PARK HOLLYWOOD, FLORIDA, 33020
INTERIOR GLAZING PARTITIONS

Date: 9/8/2024
Scale: AS SHOWN
Drawn: Y. FEITO
Job:
Sheet: SD-6
Of ____ Sheets