
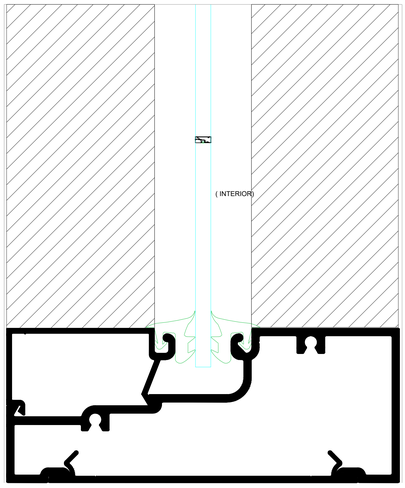



16 **Storefront Lateral Bracing Detail**

SCALE: 3" = 1'-0"

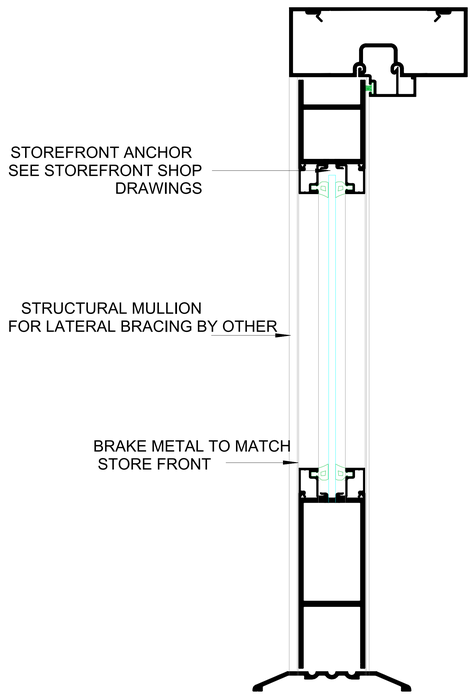

18 **Storefront Lateral Bracing Detail**

SCALE: 3" = 1'-0"

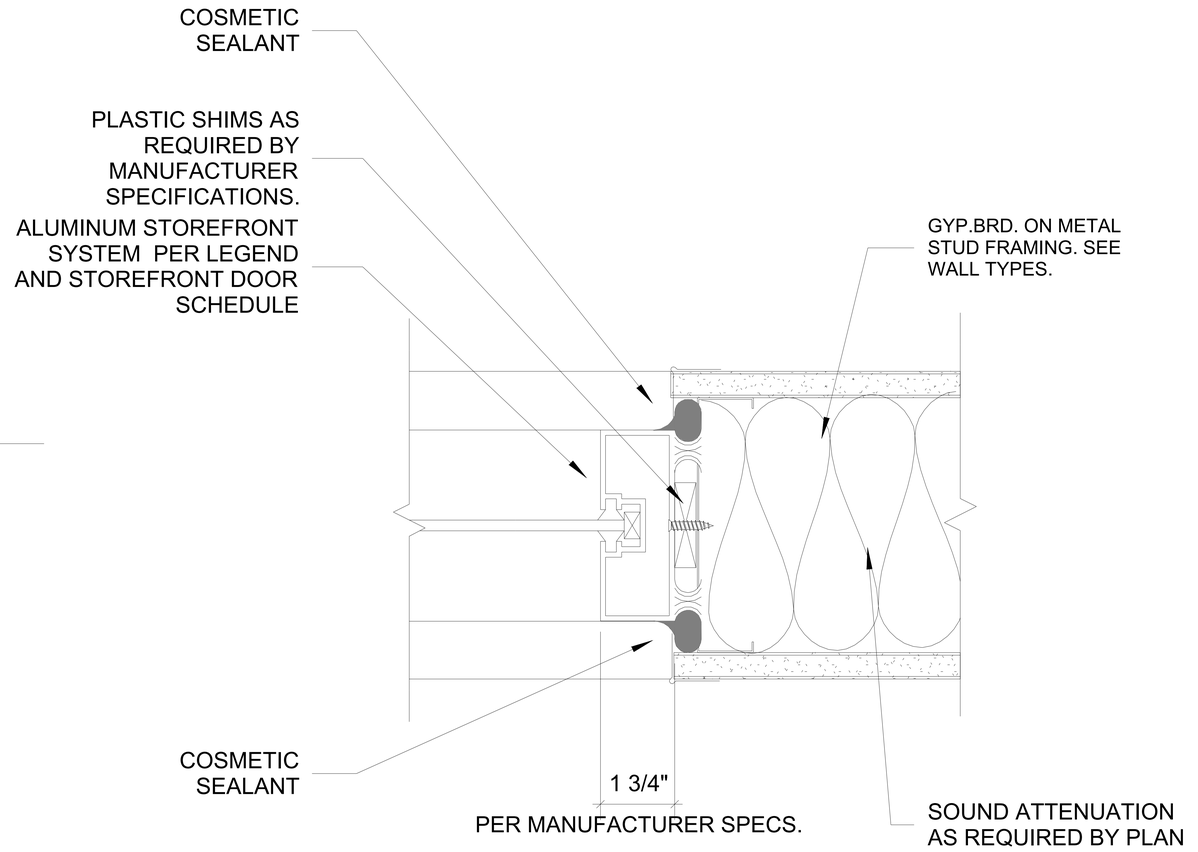

17 **Storefront Jamb -Interior Wall**

SCALE: 3" = 1'-0"

REVISIONS | BY

National Glass & Construction
7781 NW 56th Street - Doral Fl. 33166
Ph. (305) 599 09 09 - Fax. (305) 591 81 88
www.natlglass.net

AM American Consulting, Inc.
10300 SW 72nd Street, Suite 455
Miami, FL 33184 / Ph (786) 219 9490
Email: contact@amamericanconsulting.com
www.amamericanconsulting.com

PROJECT: JBL ASSET MANAGEMENT TI
1818 PARK HOLLYWOOD, FLORIDA, 33020
INTERIOR GLAZING PARTITIONS

Date: 9/8/2024
Scale: AS SHOWN
Drawn: Y. FEITO
Job:
Sheet: SD-7
Of ____ Sheets